PLAN DE SYNTHESE DES DT

ENEDIS
L'ELECTRICITE EN RESEAU

ENEDIS
Direction PADS
269 Avenue Roger SALENGRO
13015 MARSEILLE

AFFAIRE ENEDIS No : DC25/071960	PMT - 2028 - CPI HTA BIG - TOURDAI - RABATAU Commune(s): MARSEILLE 05 Département: BOUCHES-DU-RHONE
Plan No : RAC-PAS-25-001971	N° de consultation du GU : 2026073000413PI1
	COORDONNES LAMBERT 93 : X : 895679.46 Y : 6246866.37 COORDONNES GPS : Longitude : Latitude :

INTERLOCUTEURS :	Nom	Téléphone	e-mail
ENEDIS	Luca GANGAROSSA	06 99 29 44 63	luca.gangarossa@enedis.fr
Bureau d'études :	FONVIEILLE INGENIERIE	04.94.63.40.17	contact.toulon@fonvieille.com
Entreprise de travaux :			

MODIFICATIONS	No	Demandées		Etablies		Vérifiées	
	Indice	Par	Le	Par	Le	Par	Le
PLAN DE SYNTHESE DES DT	1	L.G	05/08/26	F.M	05/08/26	F.I	05/08/26

APPROBATION DEFINITIVE ET CONTROLE QUALITE

BUREAU D'ETUDE			MAITRE D'OEUVRE		
Nom	Date	Signature	Nom	Date	Signature
FONVIEILLE INGENIERIE	05/08/26		Luca GANGAROSSA		

PLAN MINUTE


ENTREPRISE DE TRAVAUX	Nom	Date	Signature

IDENTIFICATION BUREAU D'ETUDE

FONVIEILLE INGENIERIE
Géomètre
Val PARC II - Bât.A - 230 Avenue de Rome - 83500 LA SEYNE SUR MER
Tél : 04.94.63.40.17 Fax : 05.53.73.50.21

Prestataire localisation réseaux
Géoréférencement & détection
BUREAU VERITAS Certification

PLANS DE LOCALISATION

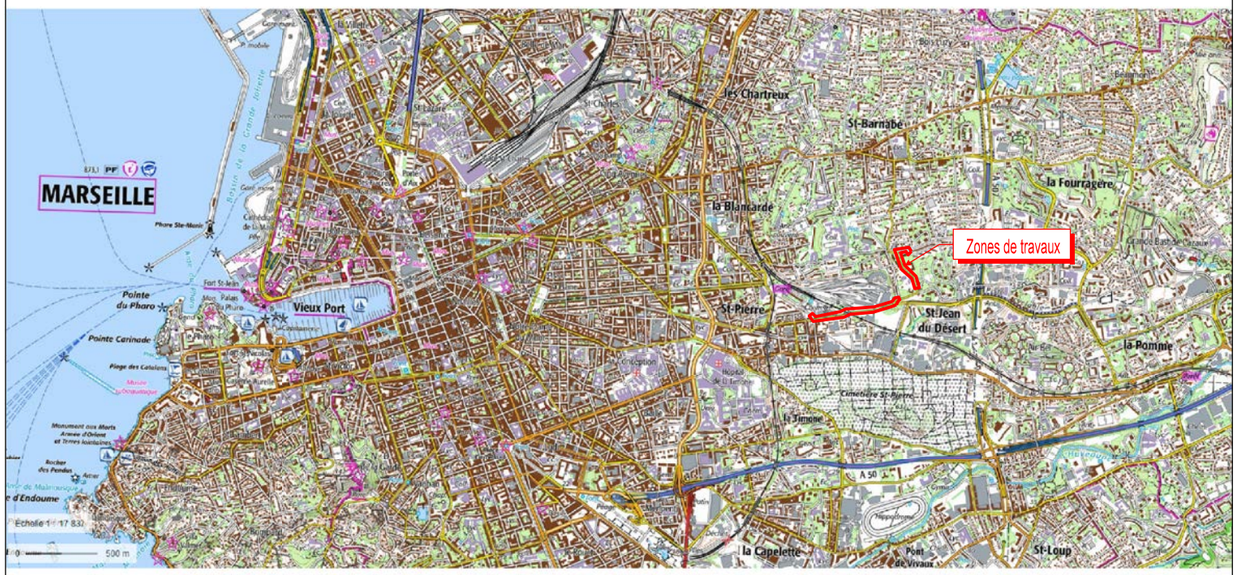

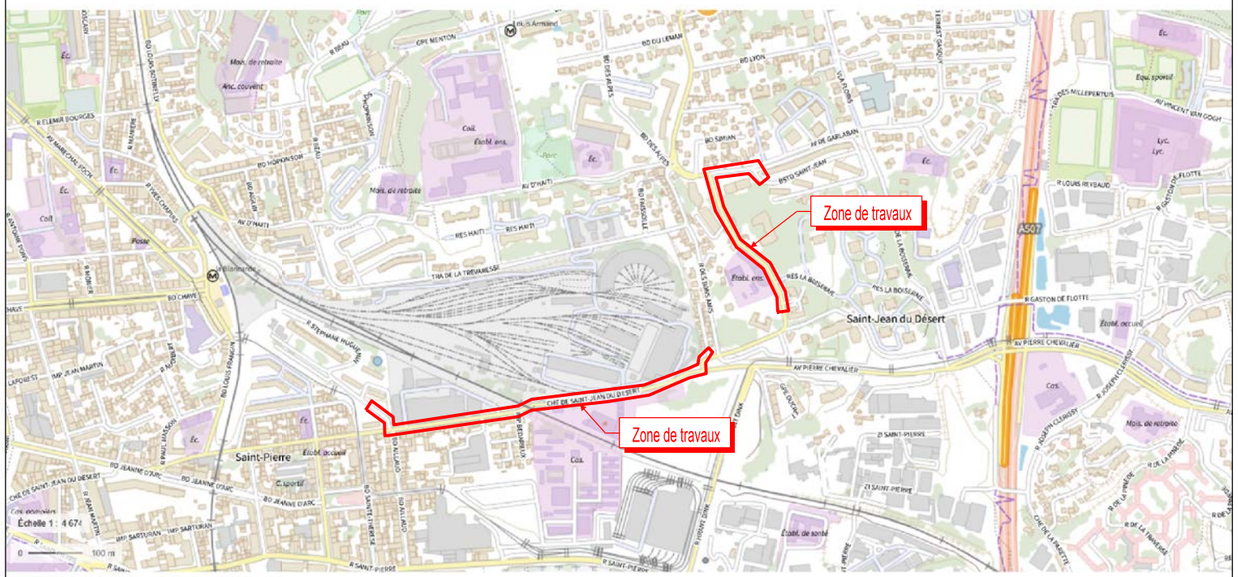


TABLEAU RÉCAPITULATIF DES DIFFÉRENTES FORMES DE PRISES DE TERRE

Coef.	A: 0,60	B: 0,17	C: 0,34	D: 0,38	F: 0,20	G: 0,24	H: 0,14	I: 0,10	J1: 0,10	J2: 0,06
Résistivité ρ en Ω . m	BFF et CE		Piquet vertical	Piquet tracteur		3m	3m 3m	5m 5m	5m 5m 5m	10m 10m 10m
	Poteau périmètre 2 m	Poste HTA/BT périmètre 10 m	Long. 3 m	Long. 3 m	Grille en tranchée 2,5 m	Serpentin 1 tranchée de 3 m Conducteur 10 m	Serpentin 2 tranchées de 3 m Conducteur 2 x 10 m	Serpentin 2 tranchées de 5 m Conducteur 2 x 15 m	Patte d'oie 3 branches de 5 m + 1 piquet central 3 m	Patte d'oie 3 branches de 10 m + 1 piquet central 5 m
50 Ω . m	30	8	17	19	10	12	7	5	5	3
100 Ω . m	60	17	34	37	20	25	14	10	10	6
200 Ω . m	120	34	66	75	40	50	28	20	20	12
300 Ω . m		50	100	112	60	75	42	30	30	18
400 Ω . m		66	133	149	80	100	56	40	40	24
500 Ω . m					100	125	70	50	50	30
750 Ω . m					150	180	105	75	75	45
1000 Ω . m					200	240	140	100	100	60

Efficace vis-à-vis des courants de foudre et à 50 Hz — Efficace seulement à 50 Hz

TABLEAU RECAPITULATIF DES VALEURS GLOBALES DU NEUTRE BT

REPERE	DATE DE LA MESURE	RESISTANCE MESUREE	OBSERVATIONS

TABLEAU RECAPITULATIF DES PRISES DE TERRE INDIVIDUELLES

REGIME DE NEUTRE : à préciser (MASSE ET NEUTRE)

REPERES	VALEUR LUE AU TELLUROHMETRE Ω . m	RESISTIVITE DU TERRAIN CALCULEE	RESISTANCE OBTENUE PAR LE CALCUL Ω .	TYPE DE TERRE ENVISAGE	RESISTANCE MESUREE APRES TRAVAUX Ω .	DATE DE LA MESURE
NEANT						

TABLEAU RECAPITULATIF DES MESURES DE COUPLAGE ENTRE LA TERRE DES MASSES ET LES TERRES DU NEUTRE

COUPLAGE ENTRE REPERES	RESISTANCE TERRE MASSE RM	RESISTANCE TERRE NEUTRE RN	RESISTANCE ENTRE MASSE ET NEUTRE RMN	RESISTANCE COUPLAGE MASSE NEUTRE RC=(RM+RN-RMN)/2	COEFFICIENT COUPLAGE MASSE NEUTRE (RC/RM)<0.15

LEGENDE des SYMBOLES et RESEAUX

SYMBOLOGIE DES OUVRAGES ET DES ACCESSOIRES

OUVRAGES AERIENS ELECTRIQUES

	EXISTANT	A CONSTRUIRE	A DEPOSER
HTB			
HTA			
BTA			
BRCHT LR	2 fils 4 fils	2 fils 4 fils	2 fils 4 fils
BRCHT DI	2 fils 4 fils	2 fils 4 fils	2 fils 4 fils
Supports	Béton/Métal Bois	Béton/Métal Bois	Béton/Métal Bois
Portiques	Béton/Métal Bois	Béton/Métal Bois	Béton/Métal Bois
Postes H61			
Interrupteurs			"Interrupteur à déposer" à ajouter dans l'étiquette du support
CMCC BT Torsadé			
Supports, Eclairage Public	ECL 2x16 Mât: Lampe:	POS ECL 2x16 Mât: Lampe:	DEP ECL 2x16 Mât: Lampe:

CLASSES DE PRECISION DES OUVRAGES SOUTERRAINS EXISTANTS OU SUITE A LOCALISATION (IC, OL, ML)

Classes	A: Présence eventuelle des PTRL (◆= Z)	B:	C:
Exemples	HTA:	BTA:	BRCHT: ? ? ?


OUVRAGES SOUTERRAINS ELECTRIQUES

	EXISTANT (A compléter avec le symbole de la classe de précision correspondante)	A CONSTRUIRE	A DEPOSER (A compléter avec le symbole de la classe de précision correspondante)
HTB	HTB 90 kV		
HTA			
BT			
BRCHT			
Eclairage Public	Ecl A	Ecl Ecl	Ecl A
Télécom Enedis			
MALT	?	Type J1	
Fourreaux, tubes, PE HD, ...			
Armoire HTA et Postes	Ajouter dans le symbole ACM ou ACT pour les armoires, PRCS ou PSSA ou PUIE ou PSSB ou PAC ou CBU pour les postes: ACM PUC	ACM PUIE	ACM PAC
Accessoires et connexions	Ajouter dans le symbole CCPI ou CCPC ou OCB ou C4 ou GPI (Piquage) ou GEt (Etoilement) ou GFC (Fausse Coupure) ou GC (Coupure): RM Jonction/Dériv. BT ou HTA PRM	RM Jonction/Dériv. BT ou HTA	RM Jonction/Dériv. BT ou HTA


AUTRES OUVRAGES EXISTANTS

Eaux Pluviales	EP B	Eaux Potable	AEP B
Télécom aérien	TéL TéL	Eaux usées	EU A
GAZ	GAZ A	Télécom souterrain (pleine terre / sous fourreaux)	TéL TéL
Fourreaux seuls		Signalisation (BT)	SL Cu B
Réseau de chaleur	CU A	Produits chimiques	PC B

ETIQUETTE SUPPORTS

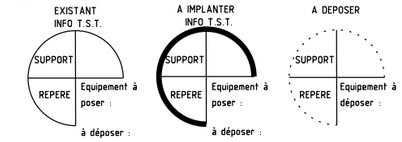

ETIQUETTES COFFRETS RESEAUX OU BRANCHEMENT

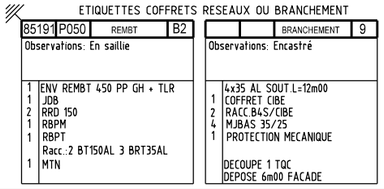

ETIQUETTE POSTE HTA/BTA

POSTE HTA/BTA : Désignation	Existant	Projeté
Type		
Puissance transfo.		
Tableau HTA		
Raccordement HTA		
Liaison transfo-tableau		
Nombre départs BTA		
Tableau BTA		
EP-Télécommandes-Divers		
Réglage prise transfo à vide		

COMMUNE: MARSEILLE

PLAN No : RAC-PAS-25-001971
AFFAIRE No : DC25/071960

PLAN D ENSEMBLE 1 / 2500 eme

N

PLAN 1

PLAN 2

PLAN 3

P0
Poste 'DESERT' n° 13205 P 5195

P1
Poste 'DESERT' n° 13205 P 1047

P2
Poste 'DEPOT' n° 13210 P 0792

P3
Poste 'CAUVIN' n° 13210 P 4187

P4
Poste 'TCHATCHE' n° 13212 P 5925

P5
poste'GARLABAN' n° 13212 P 1410

câble HTA 3x240² Al à poser

câble HTA 3x240² Al à poser

câble HTA 3x240² Al à poser

câble HTA 3x240² Al à poser

5ème arrondissement section OC

5ème arrondissement section OD

12 ème arrondissement section OA

12 ème arrondissement section OB

12 ème arrondissement section OD

Traverse de la Trévaresse

Rue du Docteur Couvin

Boulevard de la Chartreuse

Avenue

Saint-Jean-du-Désert

Chemin de

Rue Stéphane Hyguenin

Boulevard

Impasse

Rue

Hront

Place Pol Lapeyre

COMMUNE: MARSEILLE 05

PLAN No : RAC-PAS-25-001971
AFFAIRE No : DC25/071960

N

5ème arrondissement
822 section OC

12 ème arrondissement
876 section OA

FOLIO 1

FOLIO 2

FOLIO 3

FOLIO 4

FOLIO 5

Parcelle 822 C 0010
Commune de Marseille

Parcelle 822 C 0002
KALHYGE 1

P0

Poste 'DESERT' n° 13205 P 5195

câble HTA 3x240² Al à poser

câble HTA 3x240² Al à poser

câble HTA 3x240² Al à poser

P1

Poste 'DESERT' n° 13205 P 1047

5ème arrondissement
822 section OD

Parcelle 822 C 0030
LES COPROPRIETAIRES

Luquerin

Chemin de Saint Jean du Désert

Boulevard Jean Ricard

Boulevard Tramway Ligne n°1

Impasse Florensac

Impasse Florensac

Impasse Bédarrieux

Impasse

8220D

Caserne de C.R

Echelle 1/1000 - PLAN 1

0.00 50.00 100.00

COMMUNE: MARSEILLE

PLAN No : RAC-PAS-25-001971
AFFAIRE No : DC25/071960

Parcelle 876 A 0070
Les copropriétaires de la Closerie du Moulin
SAPHIE

Parcelle 876 A 0088
SNCF
SNCF

Parcelle 876 D 0179
AMP METROPOLE

FOLIO 6

FOLIO 7

FOLIO 8

câble HTA 3x240² Al à poser

P2

Poste 'DEPOT' n° 13210 P 0792

12 ème arrondissement
876 section OD

Saint-Jean-du-Desert

Chemin

Saint

Jean

du

Desert

Rue

Dink

Hrant

Bons

Amis

Echelle 1/1000 - PLAN 2

0.00 50.00 100.00

COMMUNE: MARSEILLE

PLAN No : RAC-PAS-25-001971
AFFAIRE No : DC25/071960

FOLIO 13
FOLIO 14
FOLIO 12
FOLIO 11
FOLIO 10
FOLIO 9

Parcelle 876 B 0149
Copropriétaires de l ensemble immob. sis 10 av de Garlaban

Parcelle 876 B 0052
Copropriétaires du 2 Ave de Garlaban

P5
poste'GARLABAN' n° 13212 P 1410

Parcelle 876 B 0149
Les copropriétaires res l'arte
Marignan residences

P4
Poste 'TCHATCHE' n° 13212 P 5925

Parcelle 876 A 0071
SOGIMA

Parcelle 876 A 0027
ASS CULTURELLE NOTRE DAME DES APOTRES

P3
Poste 'CAUVIN' n° 13210 P 4187

câble HTA 3x240² Al à poser

12 ème arrondissement
876 section OB

Maison de retraite Le Clos Saint-Michel

Rue du Docteur Cauvin
Boulevard de la Charbonnelle
Traverse de la Trévaresse
Rue des Bons Enfants
Impasse
Avenue
Rue
Docteur

N

Echelle 1/1000 - PLAN 3

0.00 50.00 100.00

COMMUNE: MARSEILLE

PLAN No : RAC-PAS-25-001971
AFFAIRE No : DC25/071960

Echelle 1/200 - FOLIO 1

0.00 10.00 20.00

N

Vers Folio 2

En chantier le 30.

Z=39.16 (0.85)
Z=39.16 (0.85)
Z=39.07 (0.85)
Z=38.97 (0.85)
Z=38.84 (0.85)
Z=38.77 (0.85)
Z=38.71 (0.85)
Z=38.63 (0.85)
Z=38.46 (0.85)
Z=38.41 (0.85)
Z=38.34 (0.85)
Z=38.27 (0.85)
Z=38.15 (0.85)
Z=38.14 (0.85)
Z=38.22 (0.84)
Z=38.06 (0.83)
Z=38.02 (0.85)
Z=37.97 (0.85)
Z=37.93 (0.85)
Z=38.21 (0.71)
Z=37.87 (0.85)
Z=37.86 (0.80)
Z=37.77 (0.85)
Z=37.66 (0.85)
Z=37.62 (0.85)
Z=37.59 (0.85)
Z=37.54 (0.85)
Z=37.49 (0.85)
Z=37.45 (0.85)
Z=37.44 (0.85)

HTA 240 AL P• Al::2005
HTA 3 X IX 240 AL Pi::2005
Abandonné
Abandonné
HTA 240 AL S6::Aff.053034-2024
HTA 240 AL ds FI60::2011
HTA 240 AL ds FI60::2011
HTA 240 AL P• U UNIP (TOUR D'AIGUES)::SANSANO 18/05/1967
Abandonné Teleph 56p I2/10::TROPINA 09/02/1973
Teleph HC
HTA 150 AL U TORS (ACAJOU)::1996
10 m
HTA 3x120 HC
HTA 3x120 HC
BTA 3x95Cu DETECTEE - 2019::SE2T
Abandonné HTA 3X120
Abandonné HTA 3X120
BT 95 CU - DETECTEE - 2019::SE2T
BT 4x22CU - DETECTEE - 2019::SE2T
5 TP L=14.00
0.6 m
BT 4x22Cu - DETECTEE - 2019::SE2T
BT 95 CU - DETECTEE - 2019::SE2T
2 TPC 150
Jonction
BTA 4x22
BTA 4x22
BTA 4x22
9.15 m
2.80 m
4.30 m
5.50 m
7.00 m
0.85 m
1.20 m
1.70 m
0.65 m
0.85m
5.40m
2.00m
1.35m
6.00m
4.35m
3.00m
3.10m
3.00m
0.40m
1.40m
0.60m
1.00m
TPBT 1351?
TPH L=2.00
TPC.B L=21.00m
TPC.B L=8.00m
TCB L=8.00
BT 4x44Cu AL
TéléT 4x46 AL
Capteau en briques EU 30m
TPBT L=30m
HTA

COMMUNE: MARSEILLE

PLAN No : RAC-PAS-25-001971
AFFAIRE No : DC25/071960

N

HTA 240 AL ds FI60 vers Jonction St BARNABE::20II

HTA 240 AL ds FI60 vers P.GAROUTTE::20II

HTA 240 AL ds FI60 vers P. VALLIET 20II

HTA 240 AL ds FI60 vers P.GAROUTTE::20II

HTA 240 AL ds FI60 vers P. SCARAMELLI::20II

Chemin de Saint Jean du Desert

Vers Folio 3

Vers Folio 1

Echelle 1/200 - FOLIO 2

0.00 10.00 20.00

COMMUNE: MARSEILLE

PLAN No : RAC-PAS-25-001971
AFFAIRE No : DC25/071960

N

Coupe B - B'

Vers Folio 4

Chemin de Saint-Jean du Désert

Vers Folio 2

P0
Poste 'DESERT' n° 13205 P 5195

Abandonné 3X146
Abandonné 3X146
Abandonné 3X146

Abandonné HTA
Abandonné HTA

Câble inconnu

1.00 m

47-2008-209
47-2008-209

BT 240 AL::2007

I.T.C.B L=3.00m

BT 240 AL::200

I.T.C.B L=10.00m

Abandonné 3X146 AL::96m

Caniveau en briques de 30cm

Caniveau en briques de 30cm

I.T.F L=3.50m

I.T.C.B L=2.00m

0.40m

2.50m

2.00m

0.45m

I60

I62

I74

Marseille Activité

P1
Poste 'DESERT' n° 13205 P 1047

Echelle 1/200 - FOLIO 3

0.00 10.00 20.00

COMMUNE: MARSEILLE

PLAN No : RAC-PAS-25-001971
AFFAIRE No : DC25/071960

Chemin de Saint-Jean du Désert

Vers Folio 3

Vers Folio 5

Voie ferrée (Marseille-Nice)

NOTA:"Câbles HTA" Position douteuse à cet endroit.

9.75m

2.70m

2.20m

6.65m

5.10m

2.10 m

2.00m

0.80m

0.90m

0.55m

1.05m

T.C.B L=3.00m

T.C.B L=2.00m

T.C.B L=9.00m

176

178

180

2

3

5

HTA 240 AL tpc 160::2011
HTA 240 AL tpc 160::2011
HTA 240 AL tpc 160::2011
HTA 240 AL tpc 160::2011
HTA 240 AL tpc 160::2011
BT 4x146 AL::1967

HTA Câble tr
Câble

Impasse de Bédarieu

Coupe A


N

Echelle 1/200 - FOLIO 4

0.00 10.00 20.00

COMMUNE: MARSEILLE

PLAN No : RAC-PAS-25-001971
AFFAIRE No : DC25/071960

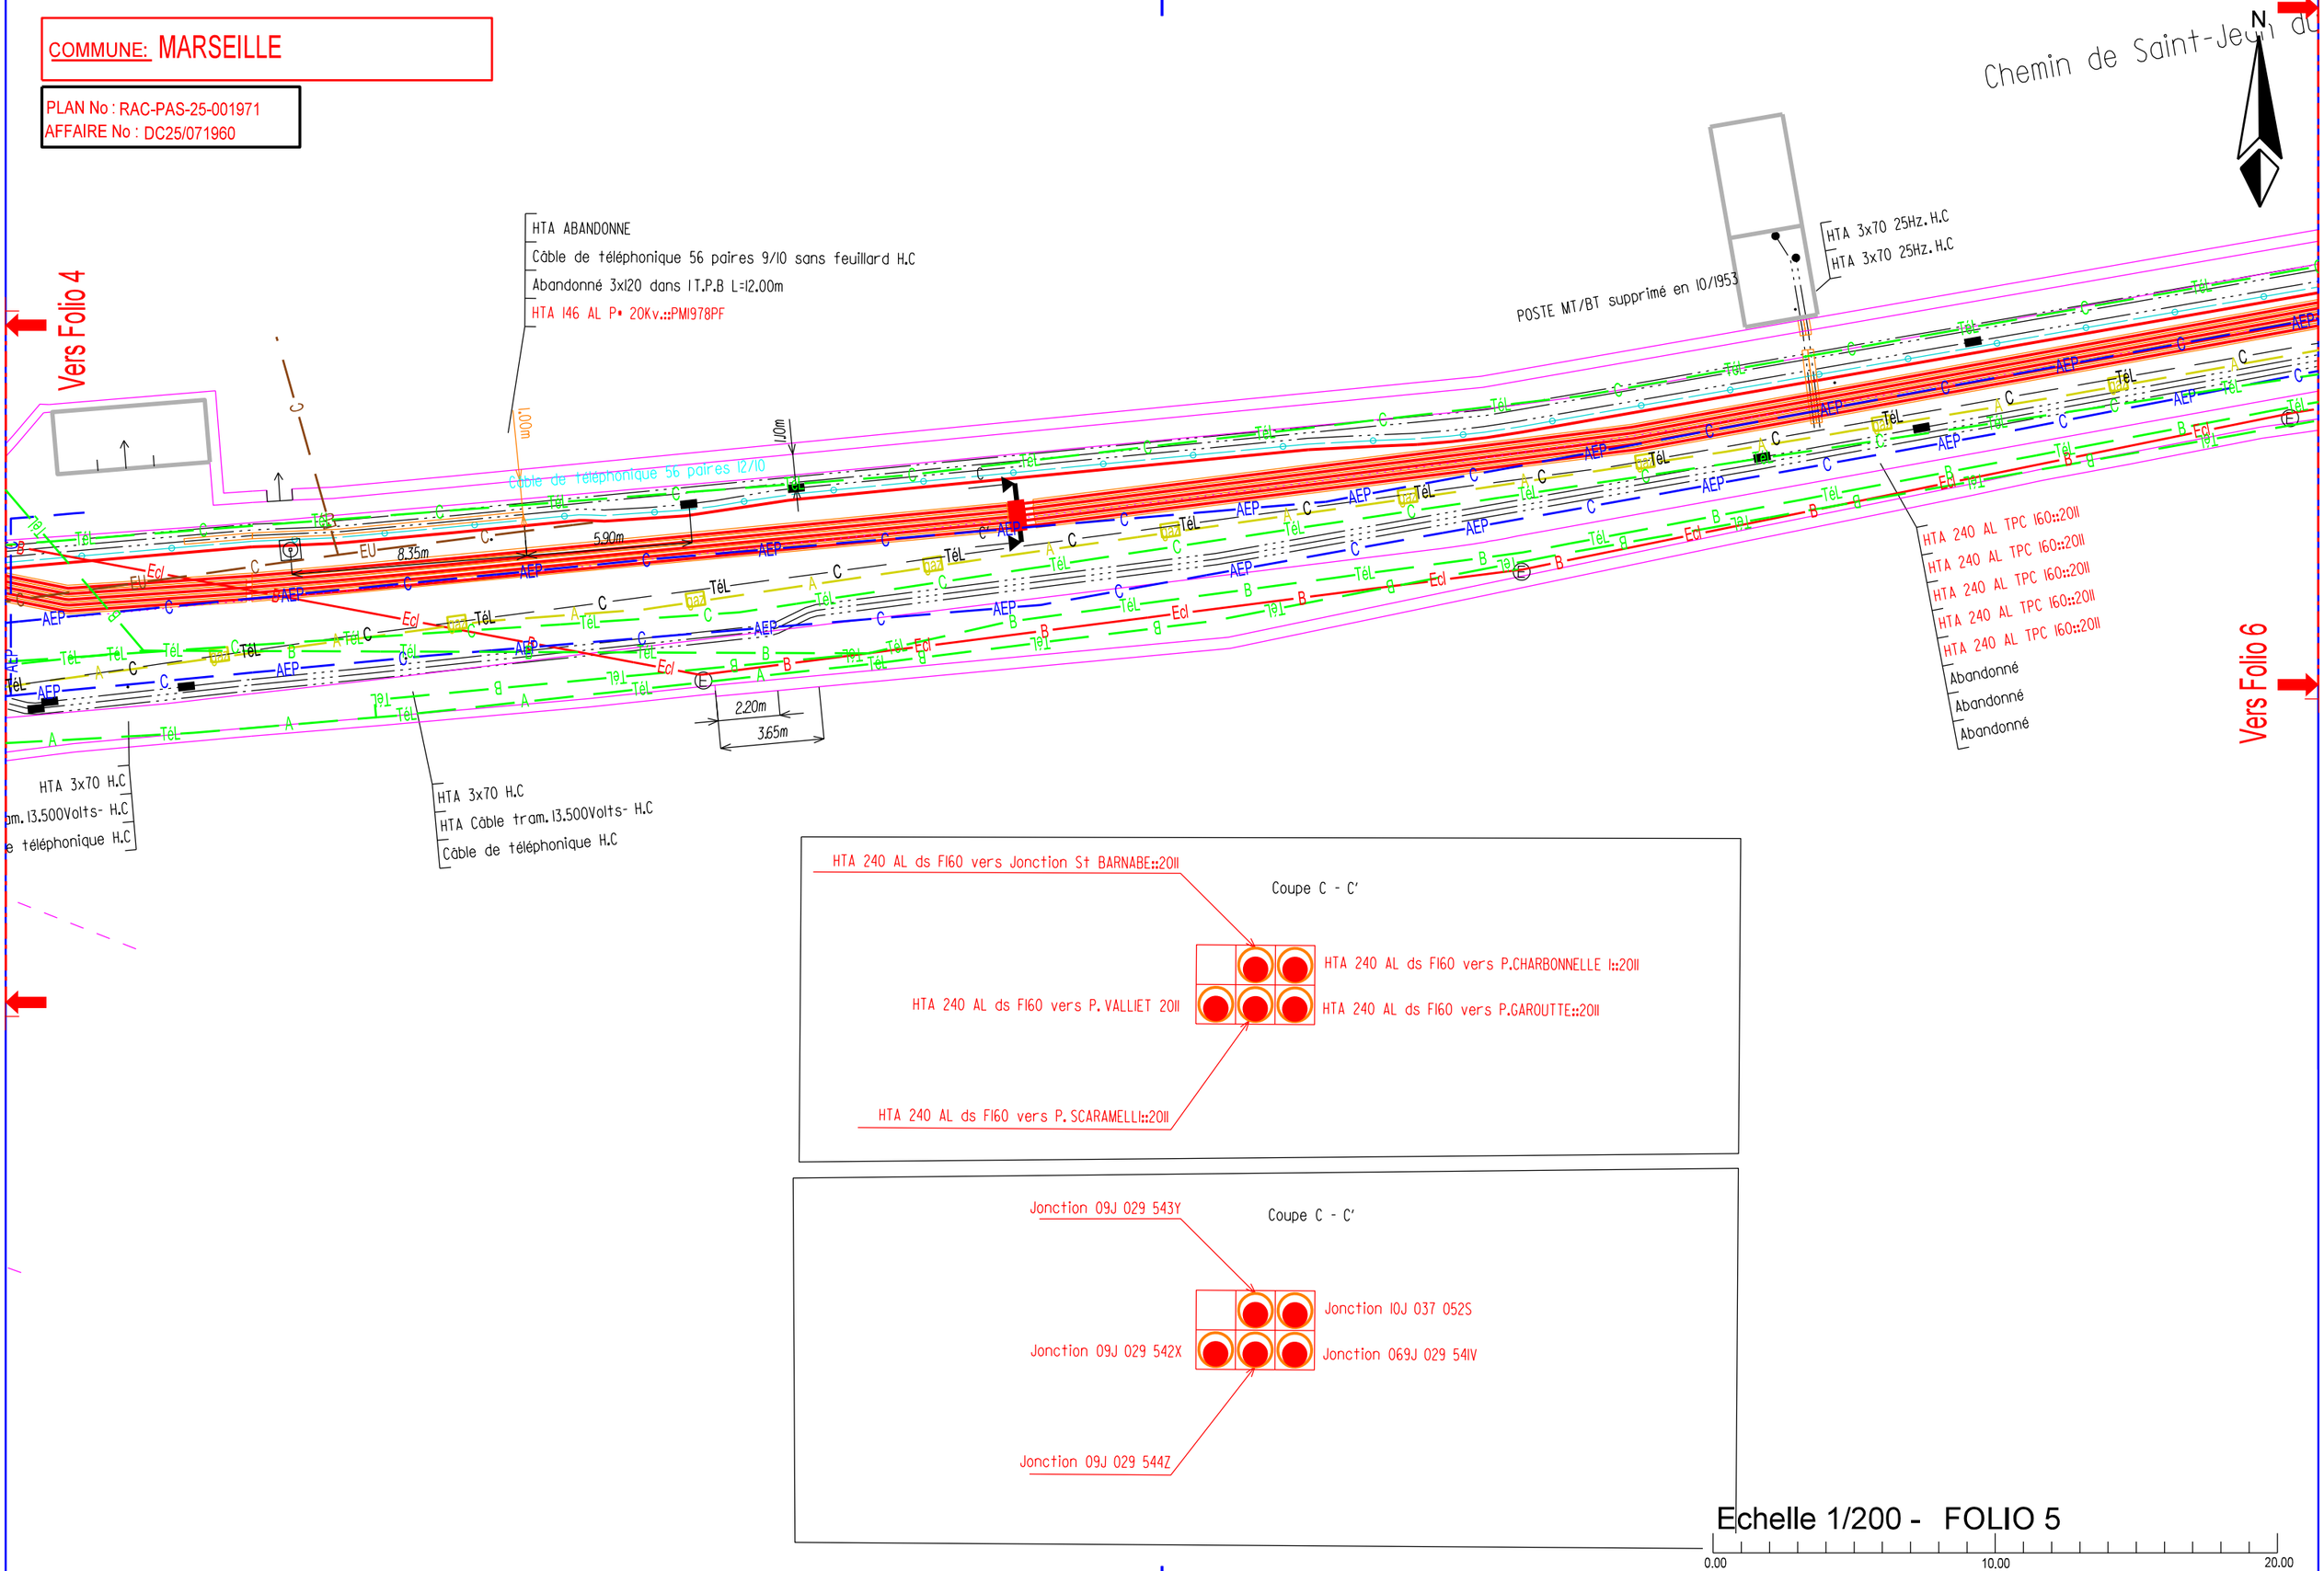

Echelle 1/200 - FOLIO 5

0.00 10.00 20.00

COMMUNE: MARSEILLE

PLAN No : RAC-PAS-25-001971
AFFAIRE No : DC25/071960

N

HTA ABANDONNE
BT ABANDONNE
HTA ABANDONNE
HTA 146 AL P• 20Kv.::PMI978PF

HTA ABANDONNE
HTA ABANDONNE
BT ABANDONNE

Désert

4.00m
0.55m
5.10m
2 T.C.B L=19.30m
Câble de téléphonique 56 paires 12/10
4.85m
6.25m
2.50m
0.90m
8.00 m
7.20 m
0.80m
HTA 146 AL P• 20Kv.::PMI972PF
Câble de téléphonique 56 paires 12/10

POSTE MT/BT
Supprimé en 11/1998

HTA ABANDONNE::Aff.RAC-PAS-25-009263-2025
HTA ABANDONNE::Aff.RAC-PAS-25-009263-2025

HTA 3x70 H.C
HTA Câble tram.13.500Volts- H.C
Câble de téléphonique H.C

Dépose POSTE COOP 13205P3456 DI

220

Vers Folio 5


Vers Folio 7

Echelle 1/200 - FOLIO 6

0.00 10.00 20.00

COMMUNE: MARSEILLE

PLAN No : RAC-PAS-25-001971
AFFAIRE No : DC25/071960

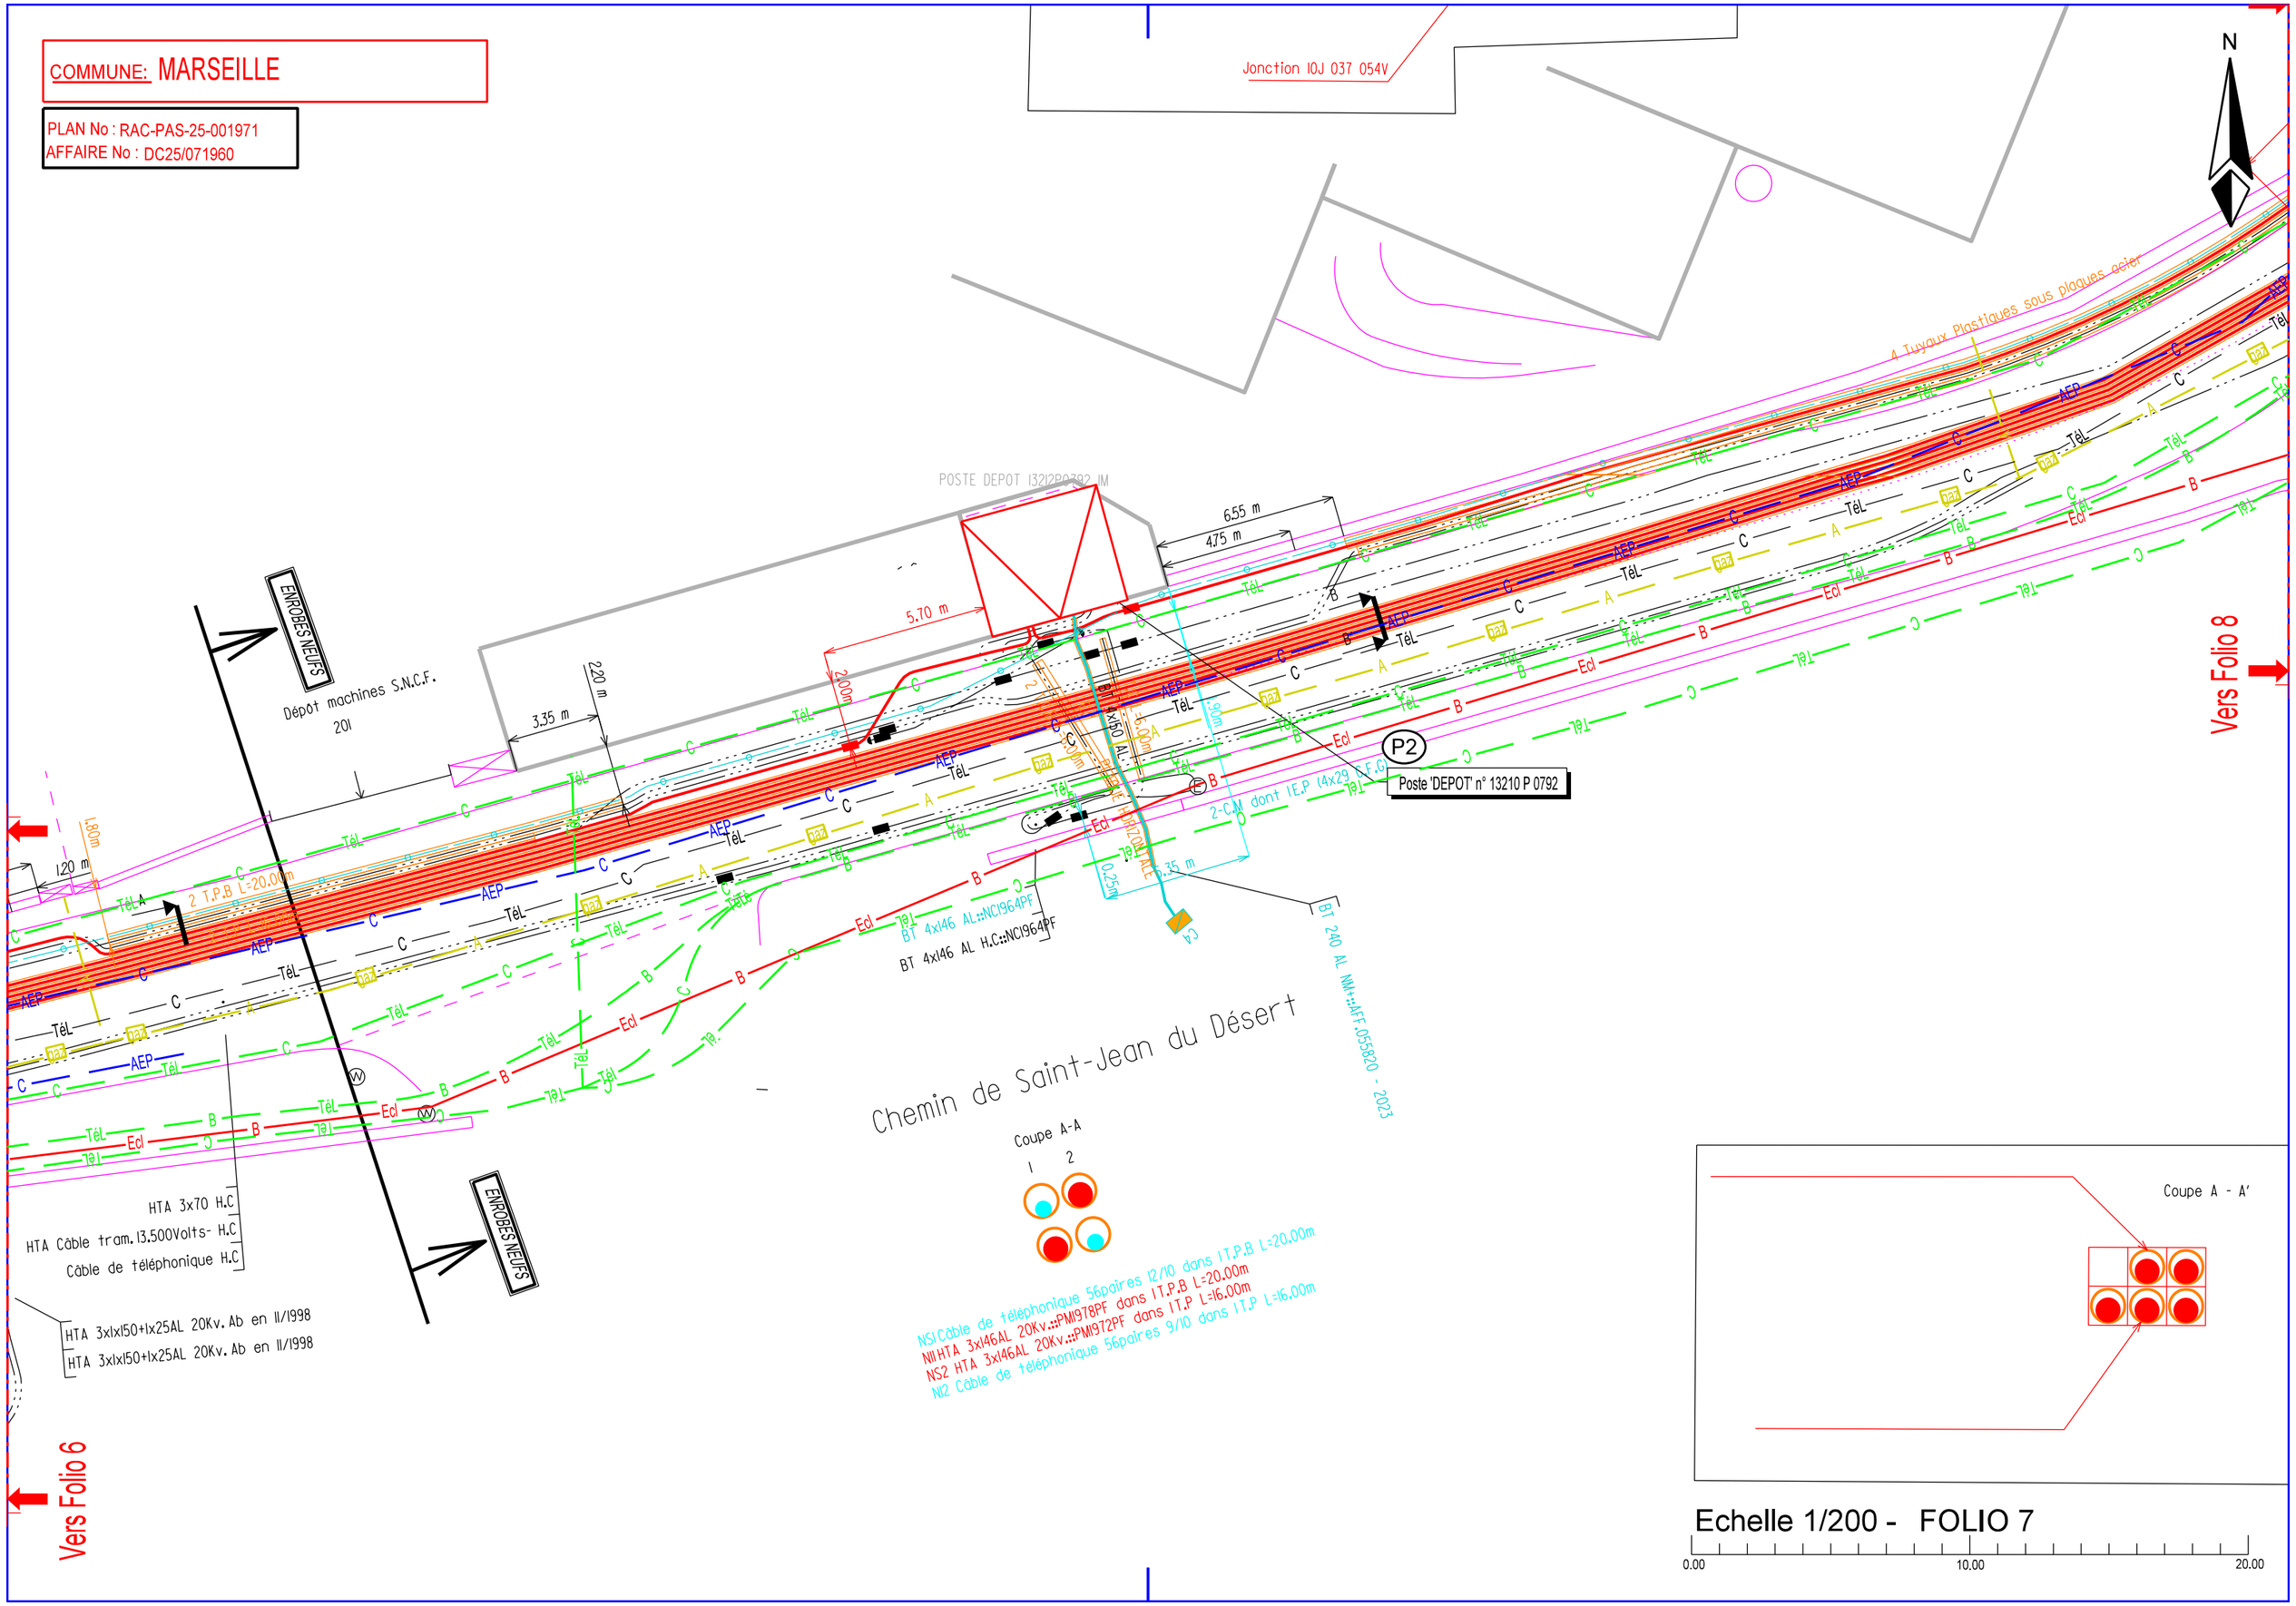

COMMUNE: MARSEILLE

PLAN No : RAC-PAS-25-001971
AFFAIRE No : DC25/071960

N

Chemin de Saint-Jean du Désert

Vers Folio 7

HTA 146 AL P•::PM 1978
HTA ABANDONNE
BT ABANDONNE
BT ABANDONNE
HTA ABANDONNE
HTA 240 AL S6::2011
HTA 240 AL S6::2011
HTA 150 AL S•::1984
HTA 240 AL S6::2011
HTA 240 AL S6::2011
HTA ABANDONNE

HTA 240 AL P•::SO 2004
HTA 240 AL P•::SO 2004

2 TPC 160 P=0.85

Telephonique 56P 12/10::1978

HTA 146 AL P•::PM 1978
HTA ABANDONNE
BT ABANDONNE
BT ABANDONNE
HTA ABANDONNE
HTA 240 AL S6::2011
HTA 240 AL S6::2011
HTA 150 AL S•::1984
HTA 240 AL S6::2011
HTA 240 AL S6::2011
HTA ABANDONNE

Abandonné 3X185AL

HTA 240 AL TPC160::2011
HTA 240 AL TPC160::2011
HTA 240 AL TPC160::2011
HTA 240 AL TPC160::2011
HTA 240 AL TPC160::2011
Abandonné::2011

HTA 240 AL P•::SO 2004
HTA 240 AL P•::SO 2004

FRICHE

VEGETATION DENSE

VEGETATION DENSE

8.45 m
3.95m
2.05m
3.80m
2.00 m
9.50 m
10.00 m
3.30 m
9.74 m
8.80 m
2.35m
2.00m
9.50m
4.92 m
4.45 m
3.45 m
3.30m
5.50 m
5.00m

Echelle 1/200 - FOLIO 8

0.00 10.00 20.00

COMMUNE: MARSEILLE

PLAN No : RAC-PAS-25-001971
AFFAIRE No : DC25/071960

Vers Folio 10

N

Echelle 1/200 - FOLIO 9

0.00 10.00 20.00

Poste 'CAUVIN' n° 13210 P 4187

POSTE CAUVIN 13212P4187 UP

HTA 3x70 Ab.
Abandonné 3X120
BT 240 AL
BT 240 AL
HTA 146 AL P• 20Kv

Abandonné 3X120

HTA 3x70 Ab.

BT 240 AL NON DETECTABLE PAS DE SIGNALITUDS

BT 95 AL

BT 150 AL

BT 2x25 CU

Groupe la Boiseraie

Rue du Docteur Cauvin

Rue du Docteur Cauvin

Câble Téléphonique Sect 0710

TP L=6.00 m

TP L=12.00

184 190 196 185 187

P3

P3

10.60 m 12.20 m 8.20 m 11.80 m

1.30 m 2.50 m 2.80 m 2.30 m 1.70 m 2.00 m 2.10 m 2.15 m 5.60 m

0.70 m 2.70 m

13J 177 11TN 13J 177 16K

HTA 150 AL

COMMUNE: MARSEILLE

PLAN No : RAC-PAS-25-001971
AFFAIRE No : DC25/071960

Echelle 1/200 - FOLIO 10

0.00 10.00 20.00

Vers Folio 11

N

Rue du Docteur Cauvin

4,55 m
3,40 m
3,00 m
2,60 m
2,40 m
4,00 m
6,20 m

BT 4x38 AL Ab.
4,40 m
5,00 m
8,90 m
5,20 m
BT 4x38 AL Ab.

HTA 3x150 Ab.
HTA 3x70 Ab.
HTA 3x70 Ab.
2 TP L=8,00 m
Câble téléphonique 54dp 12/10
6,00 m
0,20 m
BT 240 AL
BT 240 AL
Abandonné 3x120 AL
HTA 146 AL P• 20Kv
6,85 m
0,20 m

Vers Folio 9

Vers Folio 12

Abandonné 3x120 AL

HTA 146 AL P• 20Kv

HTA 3x70 Ab.

2 TP

AEP

090 m

095 m

100 m

295 m

055 m

115 m

HTA 3x70 Ab.

TT L=5.00 m

TJ 053 070M::2017

TJ 053 069K::2017

Rue du Docteur Cauvin

Plaque acier

HTA 240 AL S6::AFF0I7094-2017

Câble fibre optique

BT 240 AL NM+::2017

BT 240 AL NM+::2017

BT 240 AL NM+::2017

Z=70.25(0.85) Z=70.32(0.85)

Z=70.33(0.85) Z=70.31(0.80)

Z=70.44(0.85)

Z=70.56(0.85)

Z=70.64(0.80)

Z=70.71(0.80)

Z=70.73(0.80)

Z=70.79(0.80)

Z=70.93(0.80)

Z=71.28(0.80)

Z=71.24(0.20)

Z=71.24(0.70)

Z=71.08(0.70)

Z=71.09(0.70)

Z=71.18(0.70)

Z=71.41(0.70)

Z=71.53(0.70)

Z=71.23

Z=71.25

Z=71.43

Z=71.30

Z=70.11(0.80)

Z=70.28(0.80)

Z=70.60(0.80)

Z=70.69(0.85)

Z=70.72(0.85)

Z=70.74(0.85)

Z=70.80(0.85)

Z=70.87(0.85)

Z=70.96(0.85)

Z=72.00

Z=71.08(0.85)

Z=71.19(0.85)

Z=71.26(0.70)

Z=71.25(0.20)

Z=71.18(0.25)

Z=71.38(0.70)

Z=71.19(0.70)

Z=71.25(0.70)

Z=71.32(0.70)

Z=71.18(0.70)

Z=71.24(0.70)

Z=71.38(0.70)

Z=71.36(0.70)

POSTE TCHATCHE 13212P5925 IM

4 TPC 160 en attente

TPC 110 en attente

P4

Poste 'TCHATCHE' n° 13212 P 5925

HTA 3x150 Ab.

Abandonné 3x120 AL

BT 240 AL

HTA 146 AL P• 20Kv

Vers Folio 10

N

COMMUNE: MARSEILLE

PLAN No : RAC-PAS-25-001971

AFFAIRE No : DC25/071960

Echelle 1/200 - FOLIO 11

0.00 10.00 20.00

COMMUNE: MARSEILLE

PLAN No : RAC-PAS-25-001971
AFFAIRE No : DC25/071960

Echelle 1/200 - FOLIO 12

0.00 10.00 20.00

N

Vers Folio 13

Rue du Docteur Cauvin

Vers Folio 11

COMMUNE: MARSEILLE

PLAN No : RAC-PAS-25-001971
AFFAIRE No : DC25/071960

N

Avenue de Garlaban

BT 4x35 AL MARQUEUR RCV::Aff.53654364-2017

HTA 146 AL P• 20Kv::PMI978PF
HTA 146 AL P• 20Kv::PMI978PF

HTA 3x182 Ab.
HTA 3x182 Ab.
HTA 3x70 Ab.
HTA 3x70

HTA 146 AL P• u

Abandonné 3x182
Abandonné 3x182

Z=73.00
Z=72.92 (0.55)
Z=72.80 (0.55)
Z=72.71

TC 3.00

0.50 m
0.50 m

Canal

Téléphone 3pp T2/70

BAT A
BAT B
2
4

BT 4x50 AL

Vers Folio 14
Vers Folio 12

Echelle 1/200 - FOLIO 13

0.00 10.00 20.00

COMMUNE: MARSEILLE

PLAN No : RAC-PAS-25-001971
AFFAIRE No : DC25/071960

Echelle 1/200 - FOLIO 14

0.00 10.00 20.00

N

Vers Folio 13

Groupe Bastide Saint Jean

poste'GARLABAN' n° 13212 P 1410

POSTE GARLABAN 1321PI40 CB

BT ABANDONNE::Aff.041308-2022

BT 4x29::NCI962PF

BT 150 AL::NCI980PF

HTA 146 AL P•::1979

BT 240 AL NM+::aff: 041308-2022

TPC 160

AEP

Tél

gaz