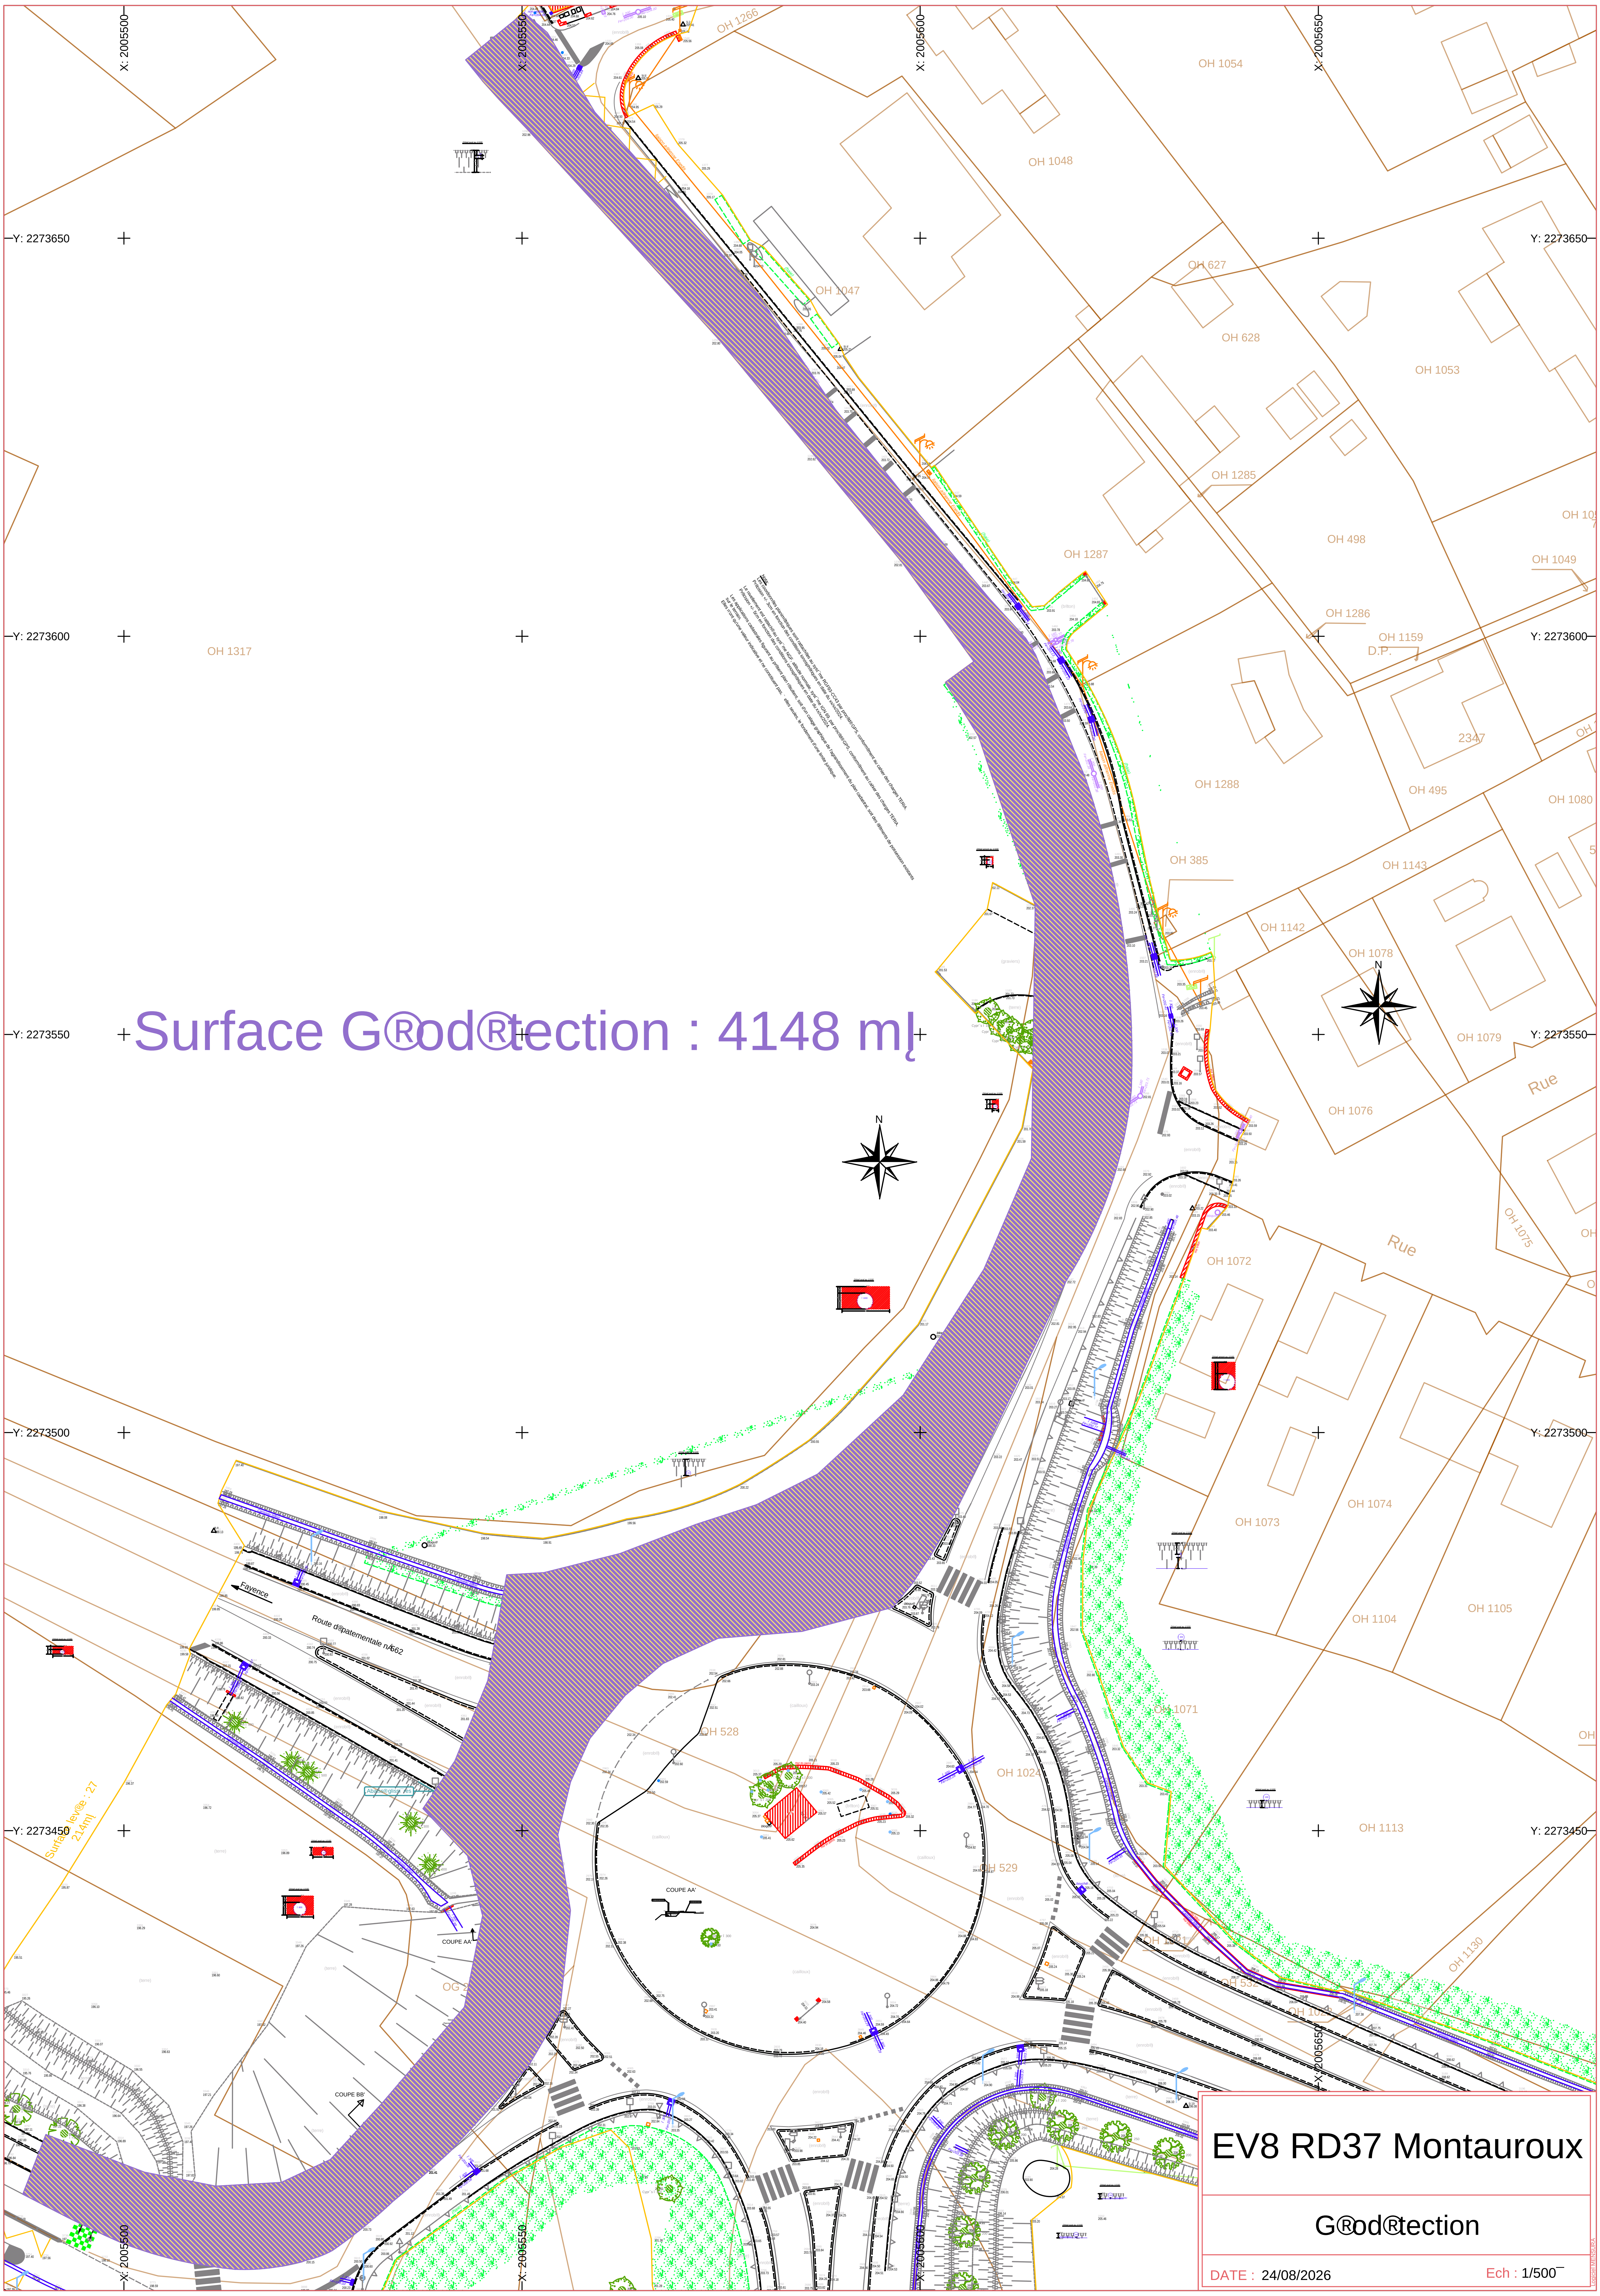
Surface G®od®tection : 4148 mļ
X: 2005500
X: 2005550
X: 2005600
X: 2005650
Y: 2273650
Y: 2273600
Y: 2273550
Y: 2273500
Y: 2273450
OH 1266
OH 1054
OH 1048
OH 1047
OH 627
OH 628
OH 1053
OH 1285
OH 1287
OH 498
OH 1049
OH 1286
OH 1159
D.P.
OH 1317
OH 1288
2347
OH 495
OH 1080
OH 385
OH 1143
OH 1142
OH 1078
OH 1079
OH 1076
Rue
OH 1075
OH 1072
OH 1073
OH 1074
OH 1104
OH 1105
OH 1071
OH 528
OH 529
OH 1113
OH 1130
OH 532
OH 1022
N
Fayence
Route départementale n°562
COUPE AA'
COUPE BB'
Caniveau béton
Surface feuille : 27 214(m)

EV8 RD37 Montauroux

G®od®tection

DATE : 24/08/2026

Ech : 1/500

Logiciel MENSURA