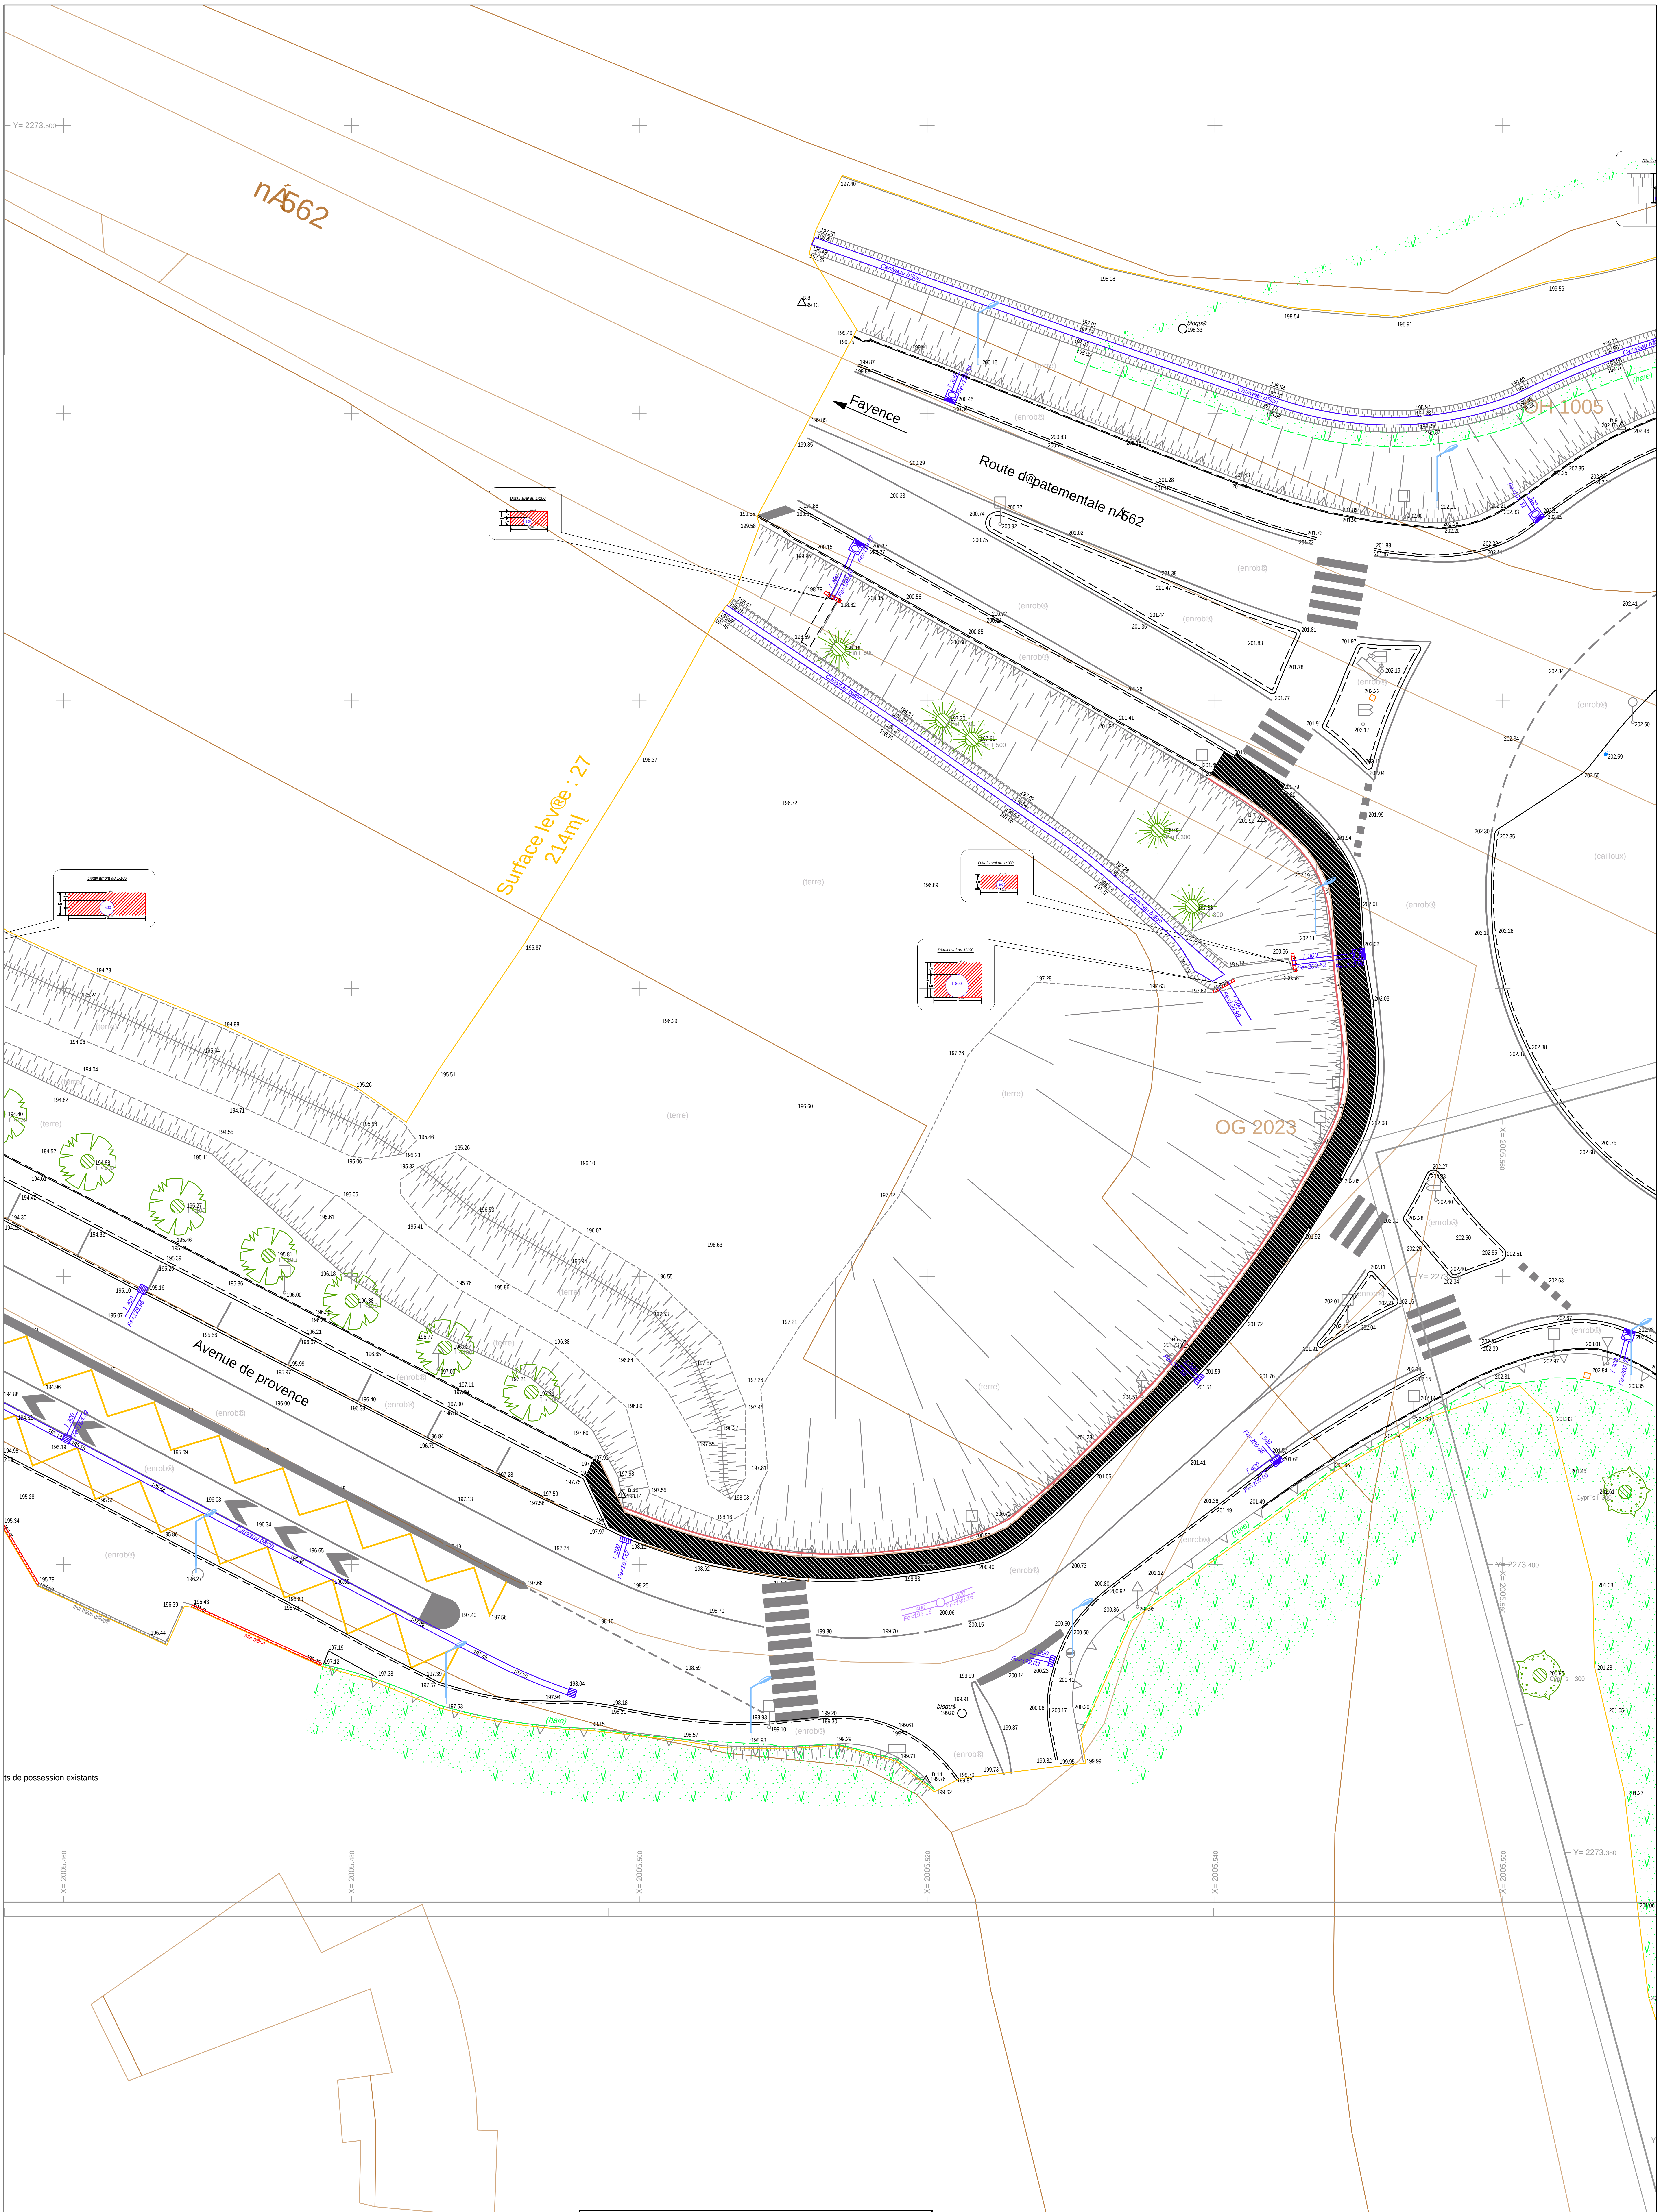
nÁ562
Surface lev®e : 27 214m]
Fayence
Route d®partementale nÁ562
OH 1005
OG 2023
Avenue de provence
(enrob®)
(terre)
(cailloux)
(haie)
bloqu®
Y= 2273.500
Y= 2273.400
Y= 2273.380
X= 2005.460
X= 2005.480
X= 2005.500
X= 2005.520
X= 2005.540
X= 2005.560
ts de possession existants

L®gende d®molition

▨	Enrob® rouge
⬚	GNT
🟥	Glissi¯res m®talliques
🟧	Bordure P1